
1-р ДАВХРЫН БАЙГУУЛАЛТ М1:200

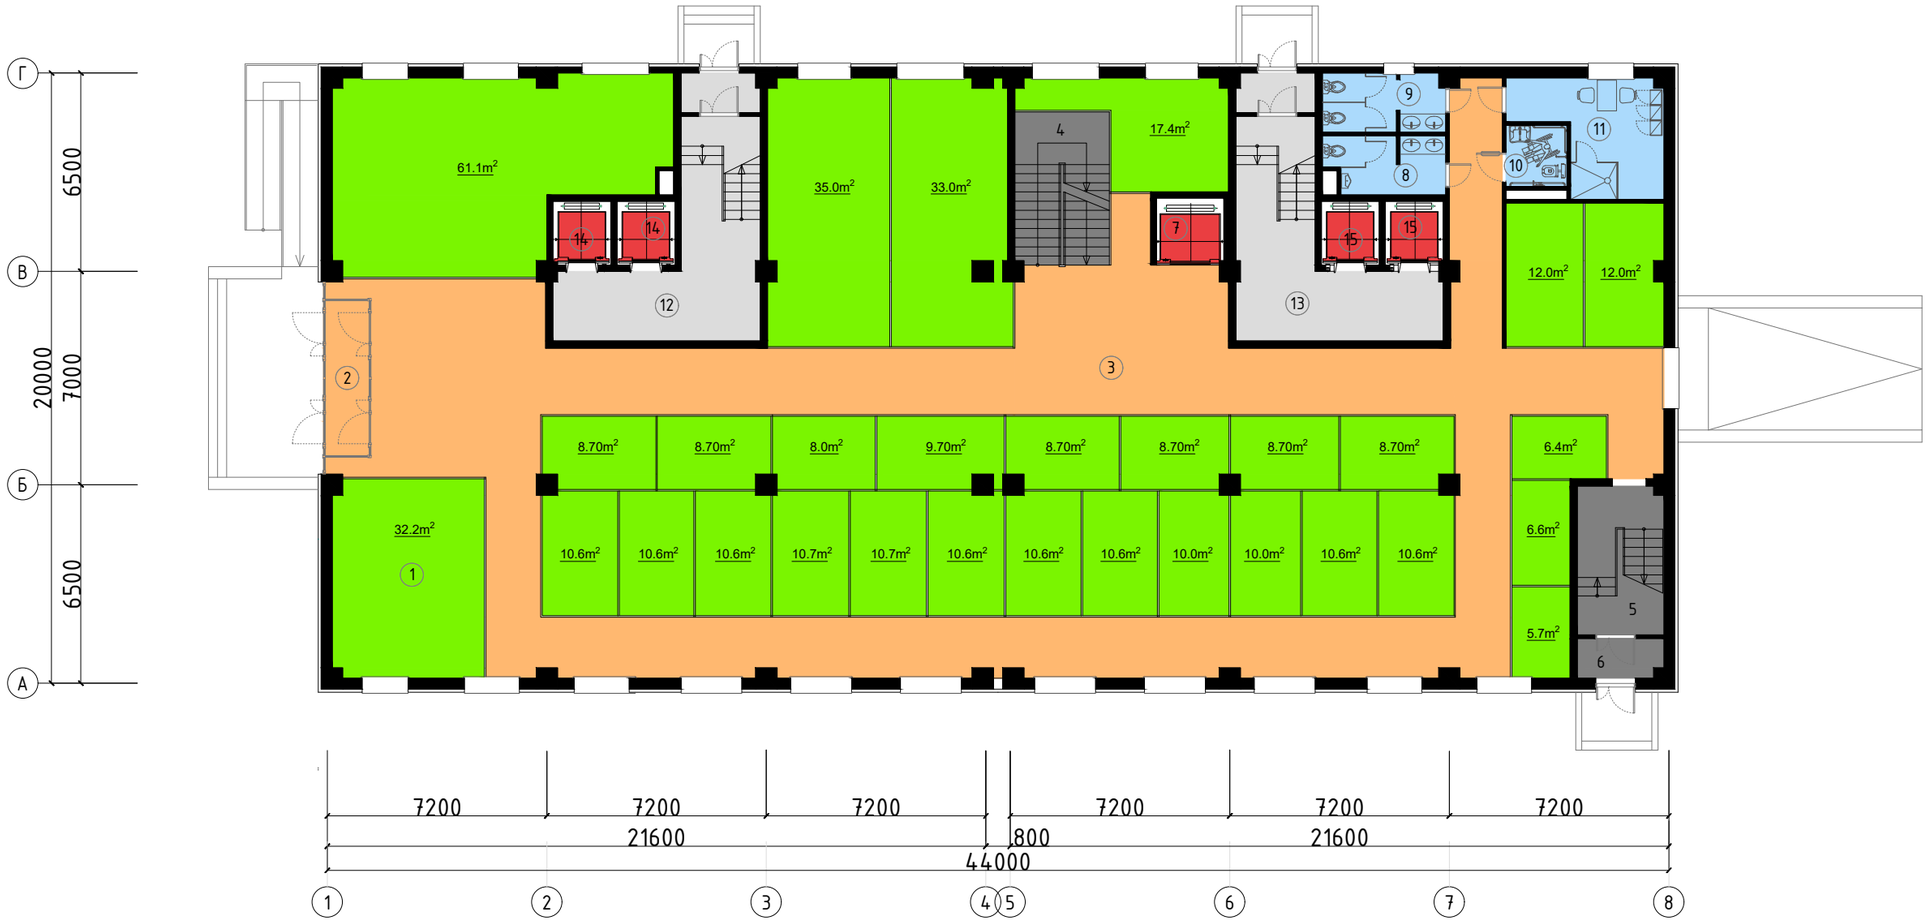

№	Өрөөний тодорхойлолт	1-р давхар m²
1	Үйлчилгээний талбай	409.64
2	Гонх	8.30
3	Нийтийн хонгил	244.23
4	Үйлчилгээний төвийн шат-1	15.54
5	Үйлчилгээний төвийн шат-2	13.75
6	Үйлчилгээний төвийн шатны Гонх	3.58
7	Үйлчилгээний төвийн Лифт	4.84
8	Нийтийн ариун цэврийн өрөө /эр/	7.17
9	Нийтийн ариун цэврийн өрөө /эм/	7.64
10	ХБИ-ний ариун цэврийн өрөө	4.00
11	Цэвэрлэгчийн өрөө, душ	15.11
12	Орон сууцны шат-1, гонх, хонгил	31.85
13	Орон сууцны шат-2, гонх, хонгил	31.85
14	Орон сууцны хос Лифт-1	7.98
15	Орон сууцны хос Лифт-2	7.98
	Нийт - 813.43	

ТӨГС ХУРЦ ХХК-ийн 195 АЙЛЫН ҮЙЛЧИЛГЭЭТЭЙ ОРОН СУУЦНЫ БАРИЛГА	НЭР	ГАРЫН ҮСЭГ	ЗАГВАР ЗУРАГ
"МОНАРЧ Констракшн" ХХК-ий захирал	Н.Бадрал		М1:150
Гүйцэтгэгч: Архитектор	Г.Саруултуяа		Хуудас 08
Захиалагч:	В.Есөнтөмөр		2022 он