11-16-Р ДАВХРЫН БАЙГУУЛАЛТ М1:200

Нийт	808.89
Тэнхлэгээр	932.74

Д/д	Өрөөний нэр	Талбай м²
1	Нийтийн хонгил	27.10
2	Шатны хонгил	16.05
3	Цахилгаан шат	3.89
4	Цахилгаан шат	4.20
	Нийт	51.24

	"Н1-Н2" айл /2 өрөө/	Талбай м²		
33	Үүдний хэсэг	3.49		
34	Ариун цэврийн өрөө	4.44		
35	Зочин, гал тогоо	32.85		
36	Унтлагын өрөө	12.15		
37	Тагт (*0.3)	0.99		
	Нийт	53.92	2	107.84

Д/д	Өрөөний нэр	Талбай м²
61	Нийтийн хонгил	28.17
62	Шатны хонгил	16.05
63	Цахилгаан шат	3.89
64	Цахилгаан шат	4.20
	Нийт	52.31

	"А" айл /3 өрөө/	Талбай м²
5	Үүдний хэсэг	5.85
6	Ариун цэврийн өрөө	4.79
7	Зочин, гал тогоо	36.19
8	Хүүхдийн өрөө	10.73
9	Унтлагын өрөө	11.55
10	Тагт (*0.3)	0.99
	Нийт	70.10


	"Б" айл /2 өрөө/	Талбай м²
11	Үүдний хэсэг	4.55
12	Ариун цэврийн өрөө	4.85
13	Зочин, гал тогоо	20.60
14	Унтлагын өрөө	14.39
15	Тагт	1.61
	Нийт	46.00

	"В" айл /3 өрөө/	Талбай м²
16	Үүдний хэсэг	8.03
17	Ариун цэврийн өрөө	4.96
18	Зочин, гал тогоо	24.98
19	Унтлагын өрөө	11.12
20	Хүүхдийн өрөө	10.70
21	Тагт (*0.3)	0.99
	Нийт	60.78

	"Л" айл /2 өрөө/	Талбай м²
56	Үүдний хэсэг	3.99
57	Ариун цэврийн өрөө	3.63
58	Зочин, гал тогоо	22.05
59	Унтлагын өрөө	9.80
60	Тагт (*0.3)	0.99
	Нийт	40.46

	"К" айл /2 өрөө/	Талбай м²
51	Үүдний хэсэг	4.22
52	Ариун цэврийн өрөө	4.25
53	Зочин, гал тогоо	22.50
54	Унтлагын өрөө	11.94
55	Тагт (*0.5)	1.88
	Нийт	44.79

	"И" айл /2 өрөө/	Талбай м²
46	Үүдний хэсэг	6.81
47	Ариун цэврийн өрөө	4.71
48	Зочин, гал тогоо	24.65
49	Унтлагын өрөө	14.79
50	Тагт (*0.5)	1.88
	Нийт	52.84

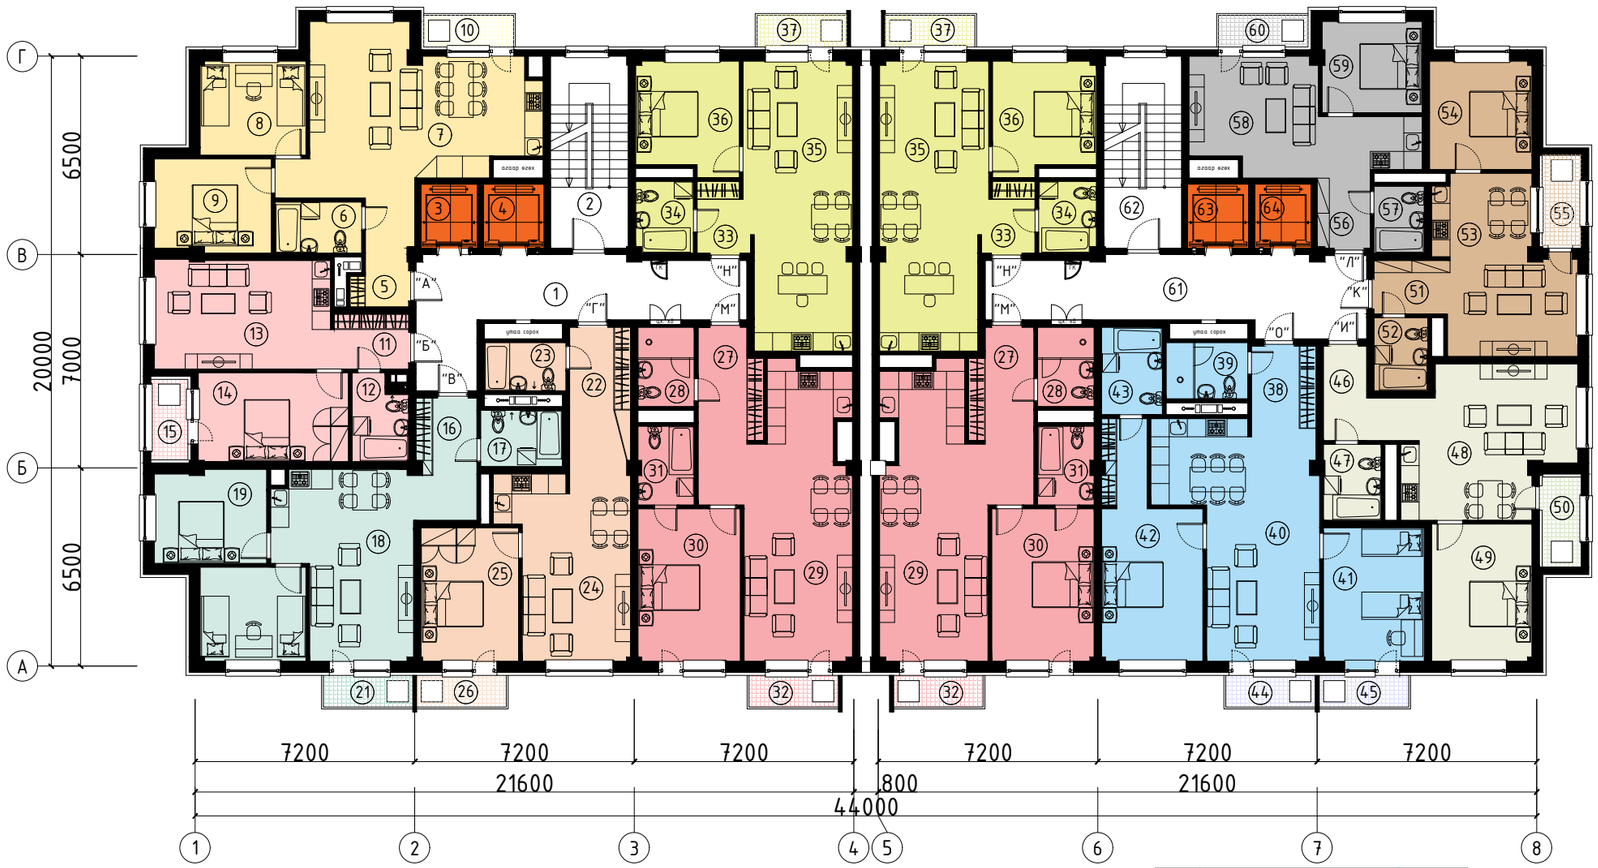

	"Г" айл /2 өрөө/	Талбай м²
22	Үүдний хэсэг	9.66
23	Ариун цэврийн өрөө	4.23
24	Зочин, гал тогоо	23.20
25	Унтлагын өрөө	14.01
26	Тагт (*0.3)	0.99
	Нийт	52.09

	"М1-М2" айл /2өрөө/	Талбай м²		
27	Үүдний хэсэг	7.61		
28	Ариун цэврийн өрөө	4.81		
29	Зочин, гал тогоо	34.38		
30	Унтлагын өрөө	16.78		
31	Ариун цэврийн өрөө	4.73		
32	Тагт (*0.3)	0.99		
	Нийт	69.30	2	138.60

	"О" айл /3 өрөө/	Талбай м²
38	Үүдний хэсэг	6.30
39	Ариун цэврийн өрөө	4.96
40	Зочин, гал тогоо	33.01
41	Хүүхдийн өрөө	14.49
42	Унтлагын өрөө	20.95
43	Ариун цэврийн өрөө	5.74
44	Тагт (*0.3)	0.99
45	Тагт (*0.3)	0.99
	Нийт	87.43

ТӨГС ХУРЦ ХХК-ийн 195 АЙЛЫН ҮЙЛЧИЛГЭЭТЭЙ ОРОН СУУЦНЫ БАРИЛГА	НЭР	ГАРЫН ҮСЭГ	ЗАГВАР ЗУРАГ
"МОНАРЧ Констракшн" ХХК-ий захирал	Н.Бадрал		М1:200
Гүйцэтгэгч: Архитектор	Г.Саруултуяа		
Захиалагч:	В.Есөнтөмөр		2023 он