4-10-Р ДАВХРЫН БАЙГУУЛАЛТ М1:200

Нийт	808.21
Тэнхлэгээр	932.74

Д/д	Өрөөний нэр	Талбай м²
1	Нийтийн хонгил	31.73
2	Шатны хонгил	16.05
3	Цахилгаан шат	3.89
4	Цахилгаан шат	4.20
	Нийт	55.87


	"Ё1-Ё2" айл /2 өрөө/	Талбай м²		
35	Үүдний хэсэг	4.00		
36	Ариун цэврийн өрөө	4.44		
37	Зочин, гал тогоо	29.03		
38	Унтлагын өрөө	12.15		
39	Тагт (*0.3)	0.99		
	Нийт	50.61	2	101.22

Д/д	Өрөөний нэр	Талбай м²
66	Нийтийн хонгил	32.80
67	Шатны хонгил	16.05
68	Цахилгаан шат	3.89
69	Цахилгаан шат	4.20
	Нийт	56.94

	"А" айл /3 өрөө/	Талбай м²
5	Үүдний хэсэг	5.85
6	Ариун цэврийн өрөө	4.79
7	Зочин, гал тогоо	36.19
8	Хүүхдийн өрөө	10.73
9	Унтлагын өрөө	11.55
10	Тагт (*0.3)	0.99
	Нийт	70.10

	"Б" айл /2 өрөө/	Талбай м²
11	Үүдний хэсэг	4.55
12	Ариун цэврийн өрөө	4.85
13	Зочин, гал тогоо	20.60
14	Унтлагын өрөө	14.39
15	Тагт (*0.5)	1.61
	Нийт	46.00

	"В" айл /3 өрөө/	Талбай м²
16	Үүдний хэсэг	8.03
17	Ариун цэврийн өрөө	4.96
18	Зочин, гал тогоо	24.98
19	Унтлагын өрөө	11.12
20	Хүүхдийн өрөө	10.70
21	Тагт (*0.3)	0.99
	Нийт	60.78

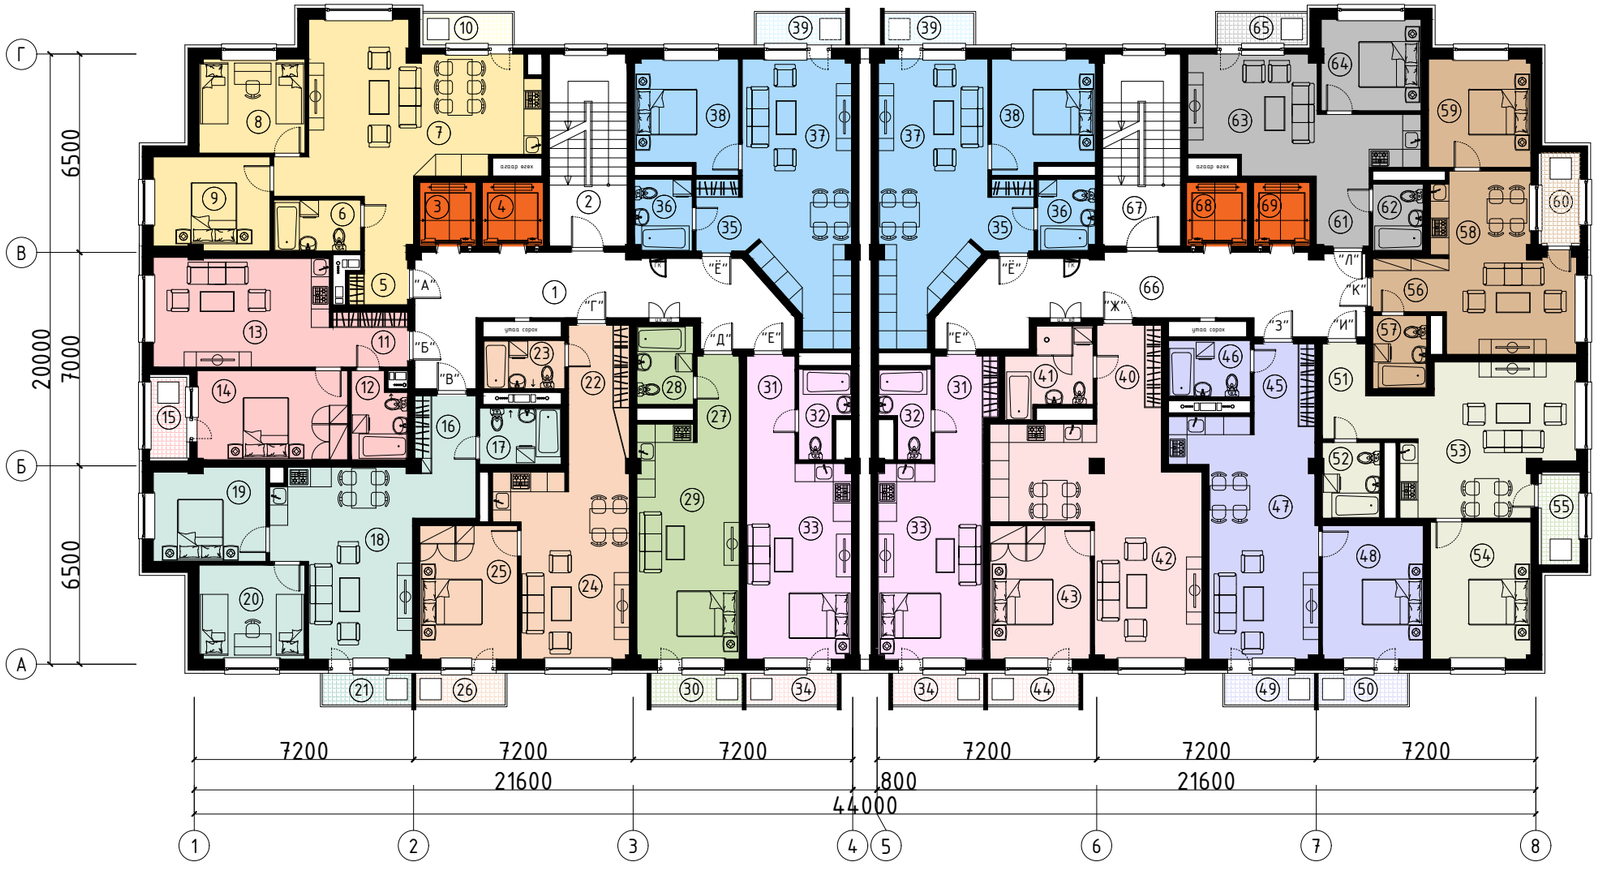

	"Л" айл /2 өрөө/	Талбай м²
61	Үүдний хэсэг	3.99
62	Ариун цэврийн өрөө	3.63
63	Зочин, гал тогоо	22.05
64	Унтлагын өрөө	9.80
65	Тагт (*0.3)	0.99
	Нийт	40.46

	"К" айл /2 өрөө/	Талбай м²
56	Үүдний хэсэг	4.22
57	Ариун цэврийн өрөө	4.25
58	Зочин, гал тогоо	22.50
59	Унтлагын өрөө	11.94
60	Тагт (*0.5)	1.88
	Нийт	44.79

	"И" айл /2 өрөө/	Талбай м²
51	Үүдний хэсэг	6.81
52	Ариун цэврийн өрөө	4.71
53	Зочин, гал тогоо	24.65
54	Унтлагын өрөө	14.79
55	Тагт (*0.5)	1.88
	Нийт	52.84

	"Г" айл /2 өрөө/	Талбай м²
22	Үүдний хэсэг	9.66
23	Ариун цэврийн өрөө	4.23
24	Зочин, гал тогоо	23.20
25	Унтлагын өрөө	14.01
26	Тагт (*0.3)	0.99
	Нийт	52.09

	"Д" айл /1 өрөө/	Талбай м²
27	Үүдний хэсэг	3.92
28	Ариун цэврийн өрөө	4.76
29	Зочин, гал тогоо	24.92
30	Тагт (*0.3)	0.99
	Нийт	34.59

	"Е1-Е2" айл /1 өрөө/	Талбай м²		
31	Үүдний хэсэг	5.58		
32	Ариун цэврийн өрөө	4.23		
33	Зочин, гал тогоо	21.99		
34	Тагт (*0.3)	0.99		
	Нийт	32.79	2	65.58

	"Ж" айл /2 өрөө/	Талбай м²
40	Үүдний хэсэг	6.87
41	Ариун цэврийн өрөө	6.88
42	Зочин, гал тогоо	36.09
43	Унтлагын өрөө	14.50
44	Тагт (*0.3)	0.99
	Нийт	65.33

	"З" айл /2 өрөө/	Талбай м²
45	Үүдний хэсэг	5.94
46	Ариун цэврийн өрөө	4.96
47	Зочин, гал тогоо	28.83
48	Унтлагын өрөө	14.50
49	Тагт (*0.3)	0.99
50	Тагт (*0.3)	0.99
	Нийт	56.21

ТӨГС ХУРЦ ХХК-ийн 195 АЙЛЫН ҮЙЛЧИЛГЭЭТЭЙ ОРОН СУУЦНЫ БАРИЛГА	НЭР	ГАРЫН ҮСЭГ	ЗАГВАР ЗУРАГ
"МОНАРЧ Констракшн" ХХК-ий захирал	Н.Бадрал		М1:200
Гүйцэтгэгч: Архитектор	Г.Саруултуяа		
Захиалагч:	В.Есөнтөмөр		2023 он